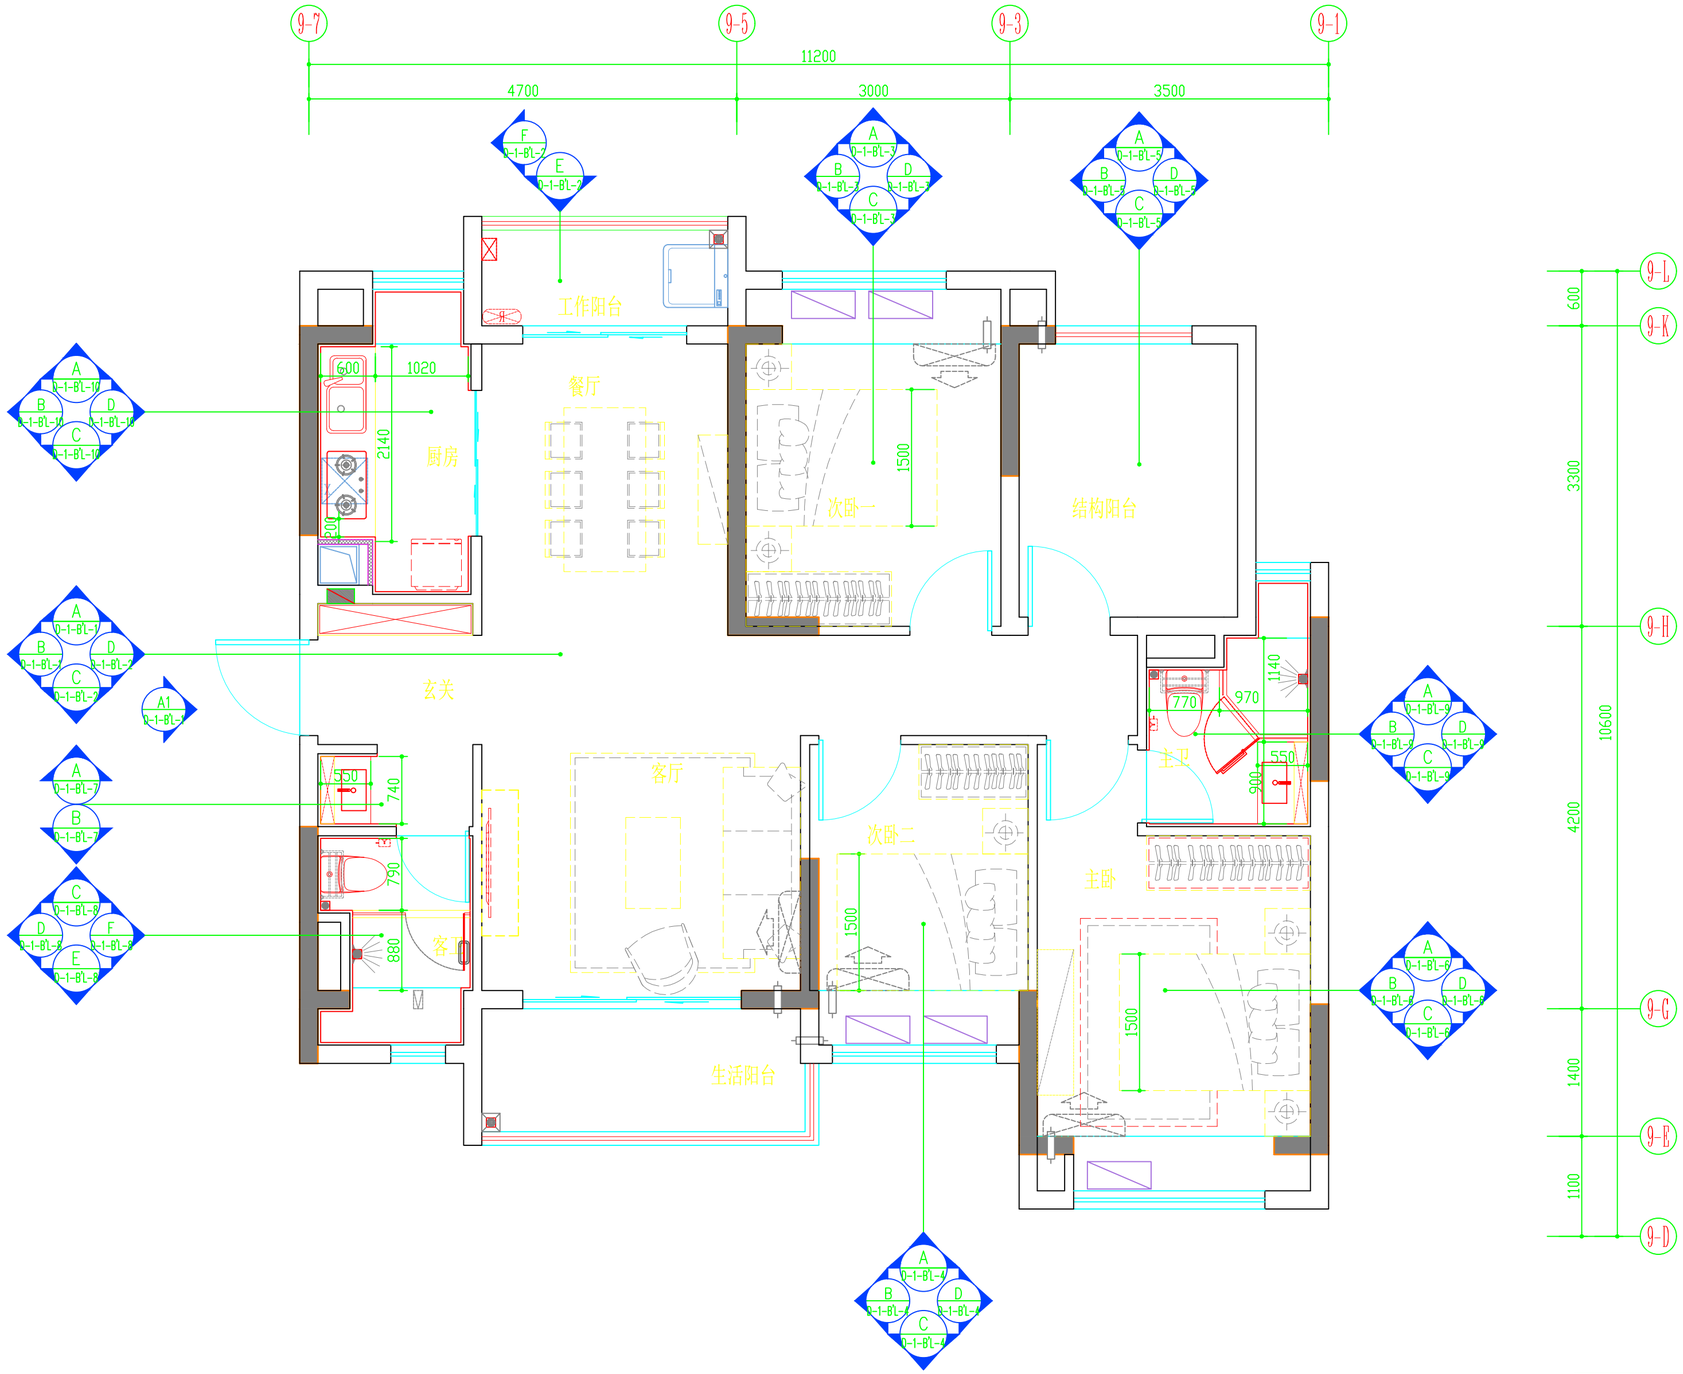

图例	说 明
⊠	燃气表
	热水器(示意)

注:1.平面虚线部分为软装选购家具。
2.如厨房尺寸满足的情况下，建议消毒柜摆放在炉头下方以外的地方。

--
D-1-9P/1-1

(T3)105㎡户型12#03单元交标大货平面布置及索引图

Scale 1 :50 (A2)